	实　名	签　名
项目负责人	张叶军	张叶军
专业负责人	张叶军	张叶军
设　计　人	徐盛华	徐盛华

注册(执业)章

中华人民共和国一级注册建筑师
姓　名:张　叶　军
注册号:3303291-003
有效期:至2025年6月4日

预留章

出图章

明珠建设集团有限公司
建筑行业建筑工程甲级;建筑行业人防工程甲级(有效期至2028年12月22日)
NO:A133032917
浙江省住房和城乡建设厅监制


审图章

浙江省建设工程施工图设计文件
(审查专用章)
审查单位:金华市南山建设工程施工图审查中心
审查范围:房建一类　　证书编号:12161
(含消防、人防、气象审查)
浙江省住房和城乡建设厅、人民防空办公室、公安消防总队、气象局监制

竣工章

图例
用地红线
拟建建筑
4M宽消防车道
停车位
消防救援口6MX6M范围线

消防车道应在明显位置设置消防车道禁停标线及路面警示标牌,尺寸规格详见浙江省消防技术规范难点问题操作技术指南2020版-浙消[2020]166号第15页

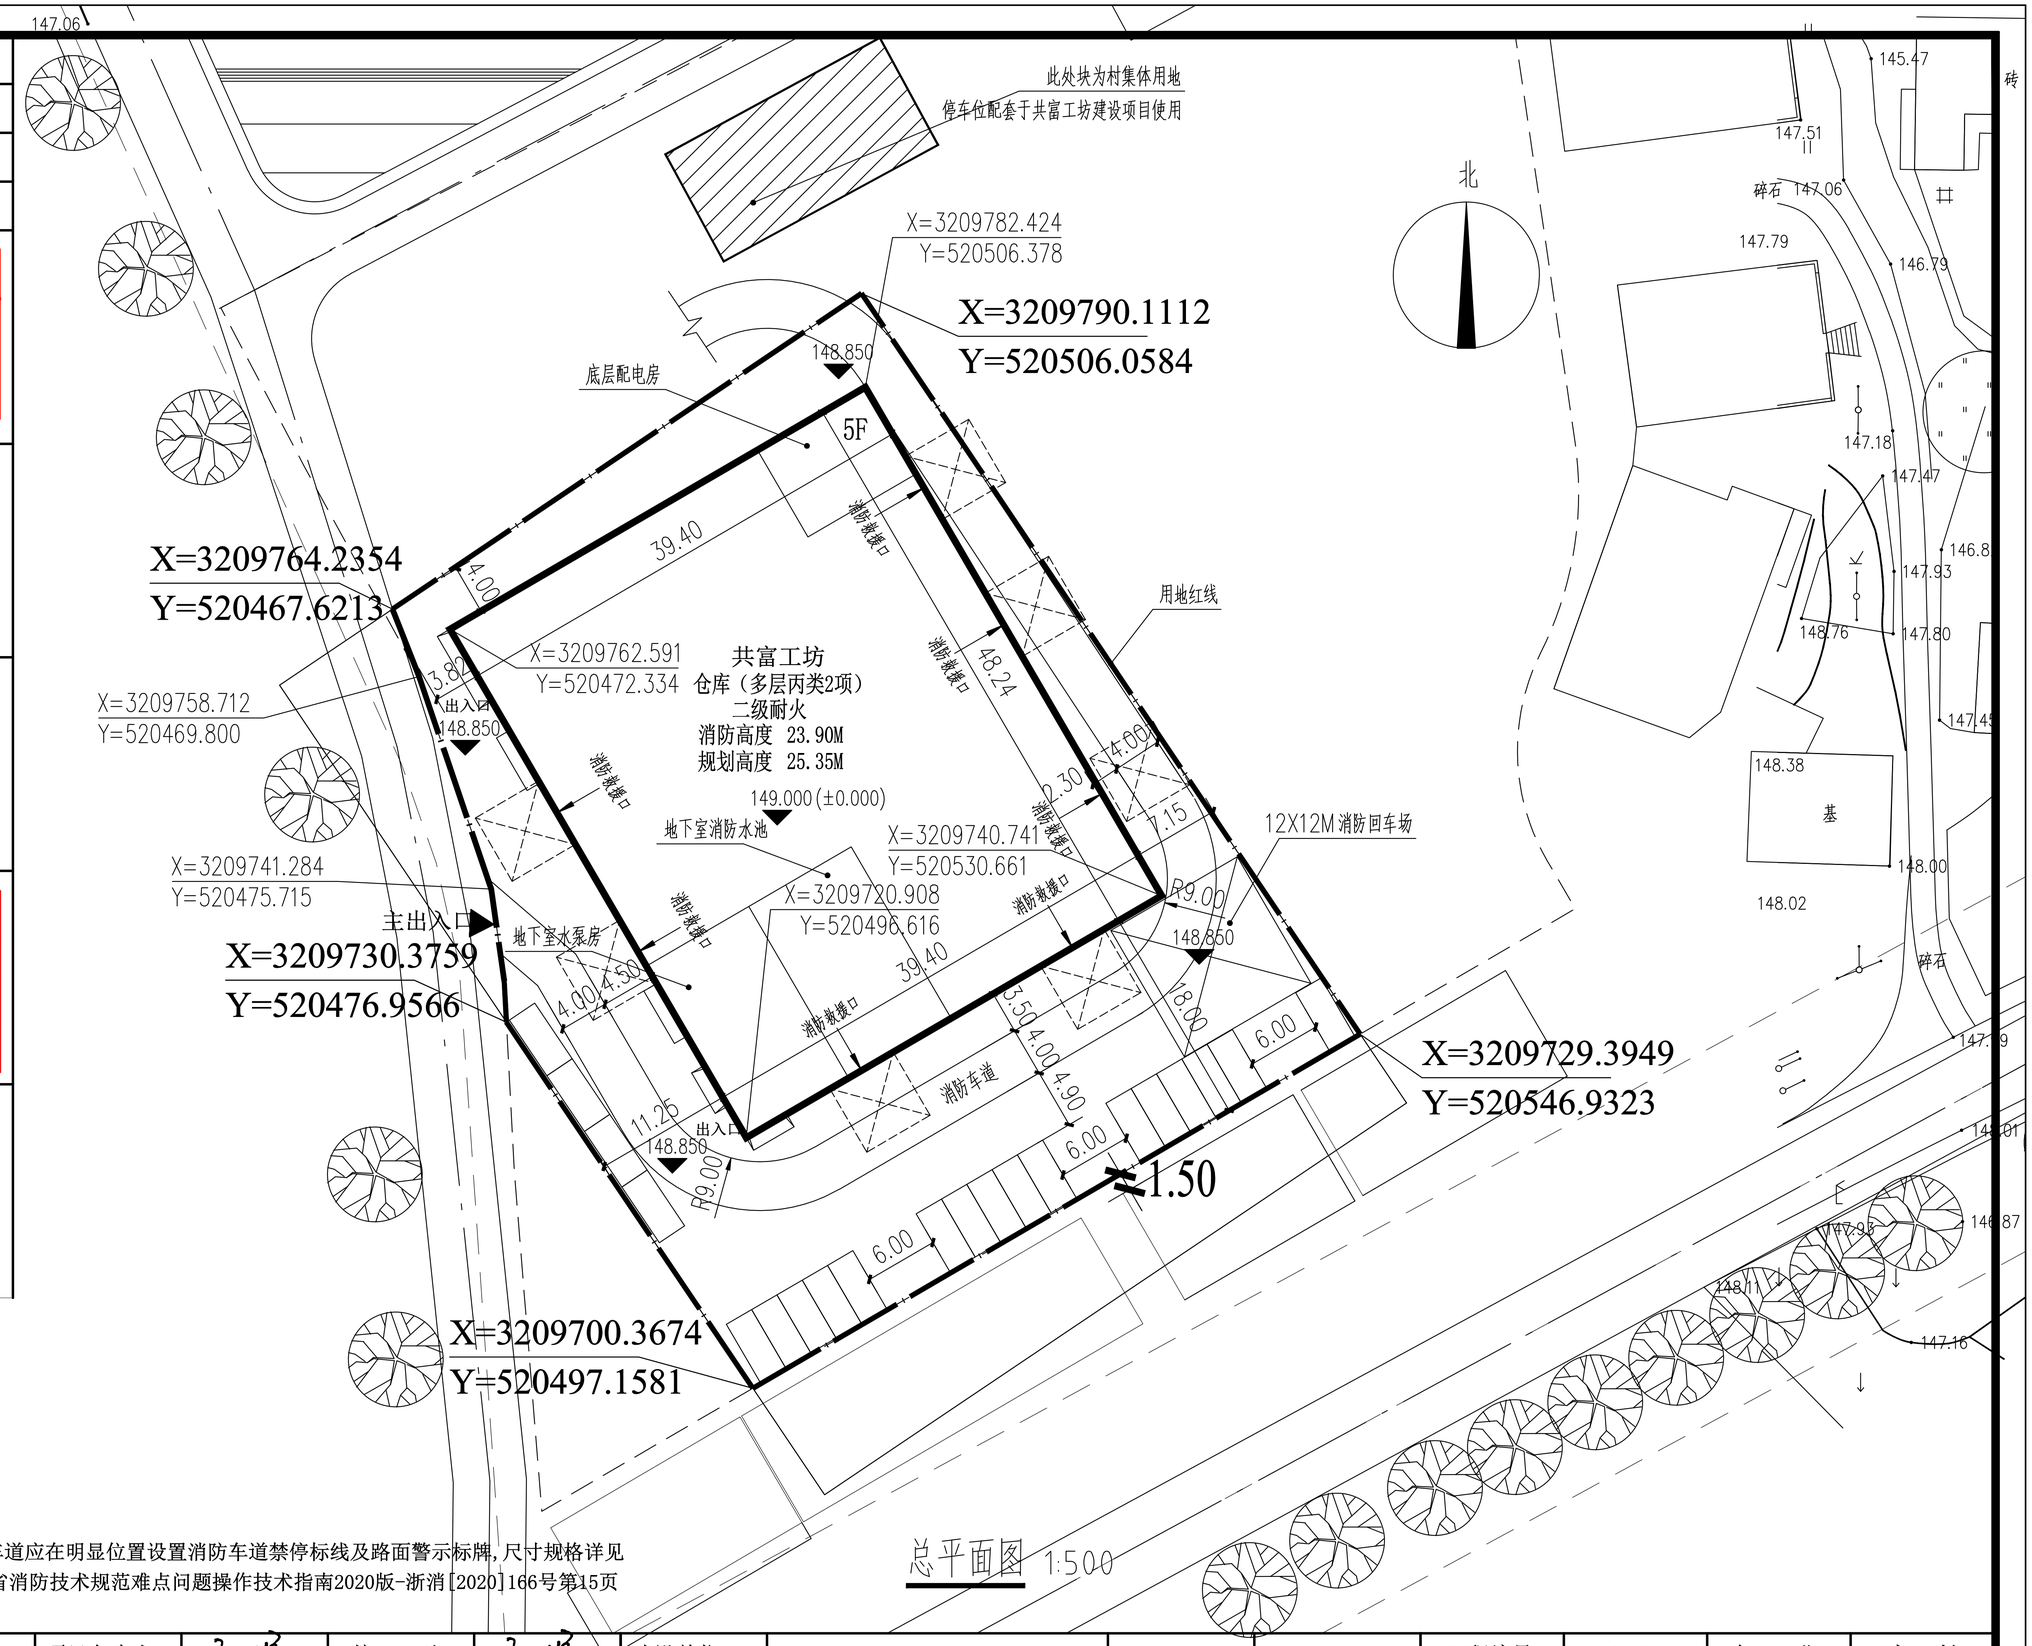

总平面图 1:500

明珠建设集团有限公司 PEARL CONSTRUCTION GROUP CO.,LTD 工程设计资质等级:建筑行业(建筑工程、人防工程)甲级; 工程设计资质证书编号:A133032917	项目负责人		校　对		建设单位	永康市龙山镇胡塘下村股份经济合作社	图　名	总平面图	工程编号	W-2024-107	专　业	建　筑
	专业负责人		审　核		项目名称	永康市龙山镇胡塘下村共富工坊建设项目			设计阶段	施工图	版 本 号	A
	设　计　人		审　定		子项目名称	仓库			图　号	01	日　期	2024.03

图纸未经施工图审查机构审查合格,不得用于工程施工.